
K31-01 低压配电箱安装接线

总开关	电涌保护	厨卫插座开关	房间插座开关	照明1	照明2

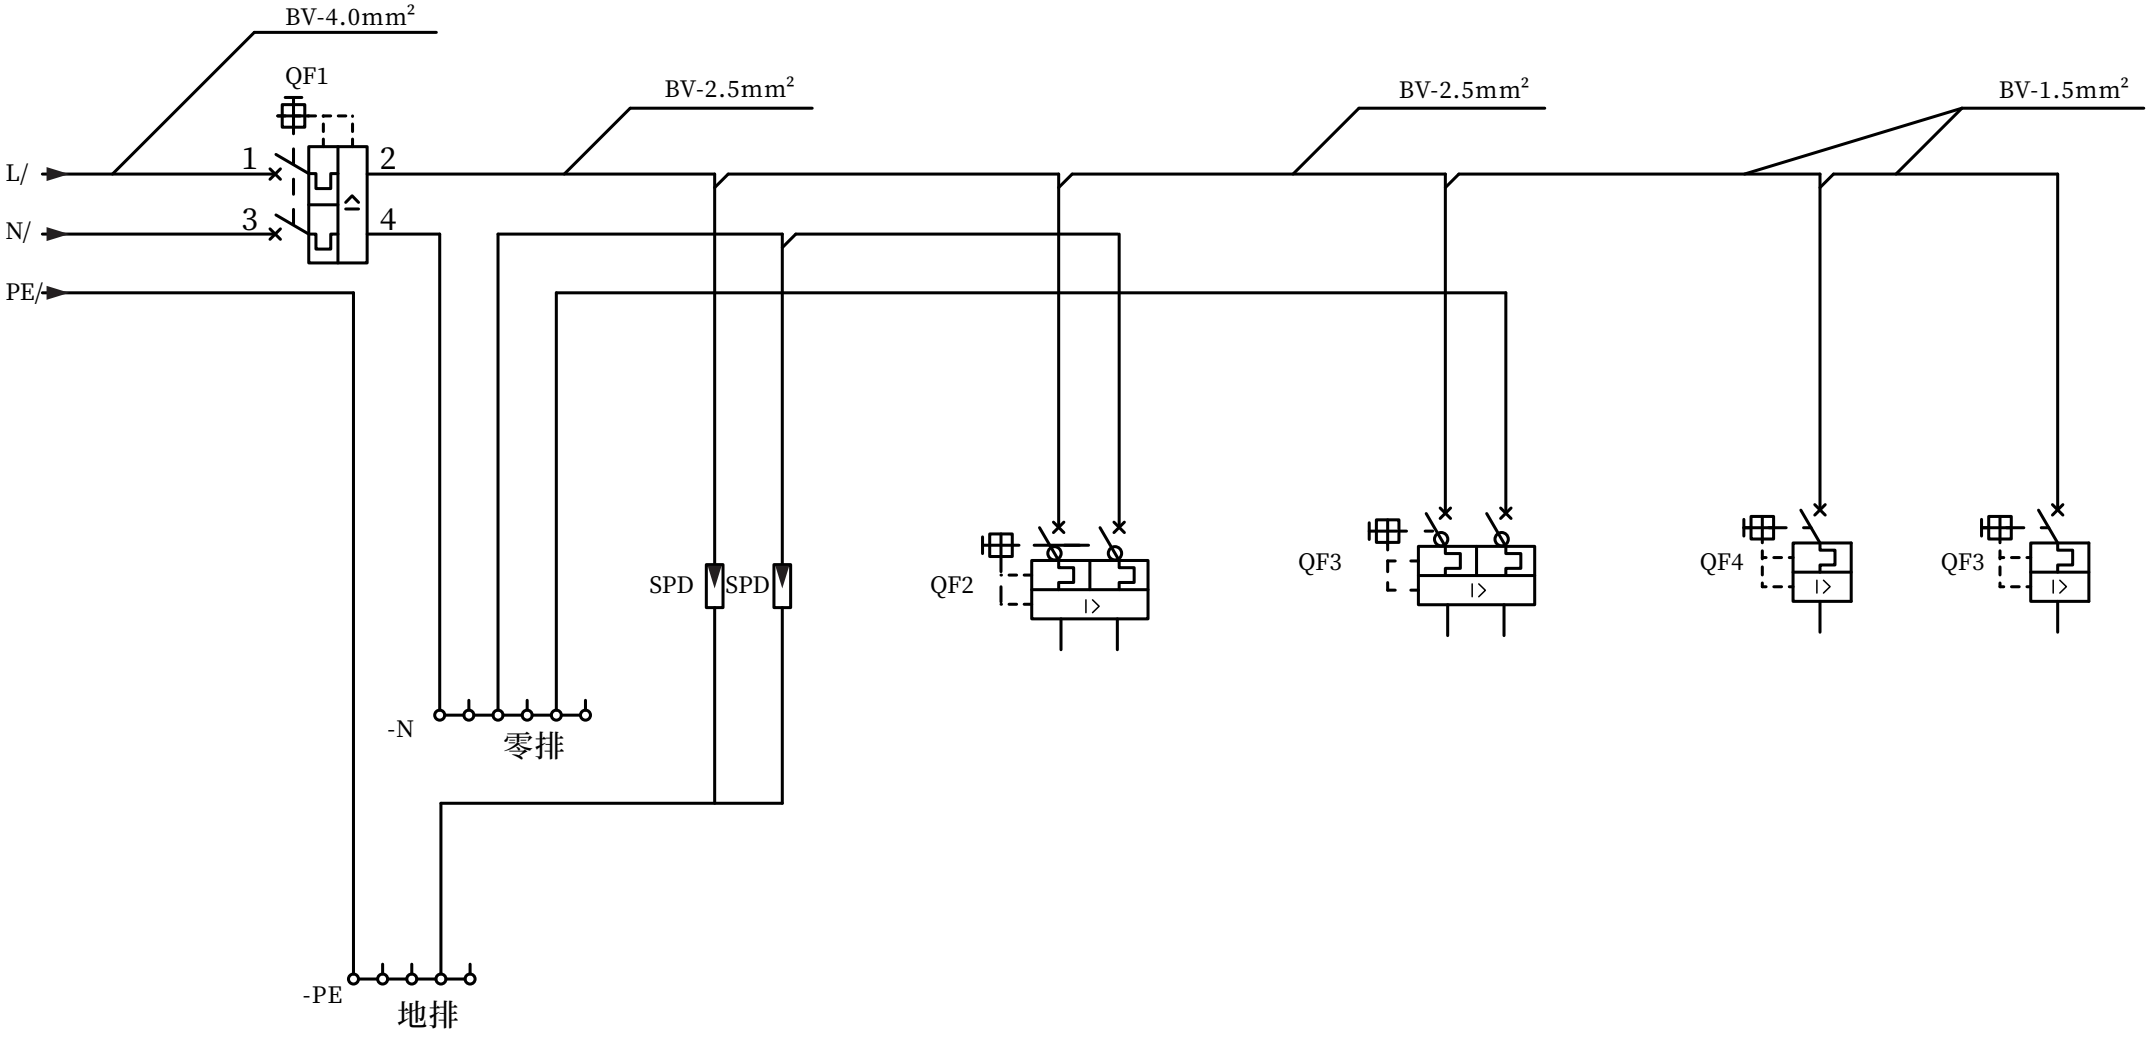

注:在接线端子上做环形端子,并用螺丝固定